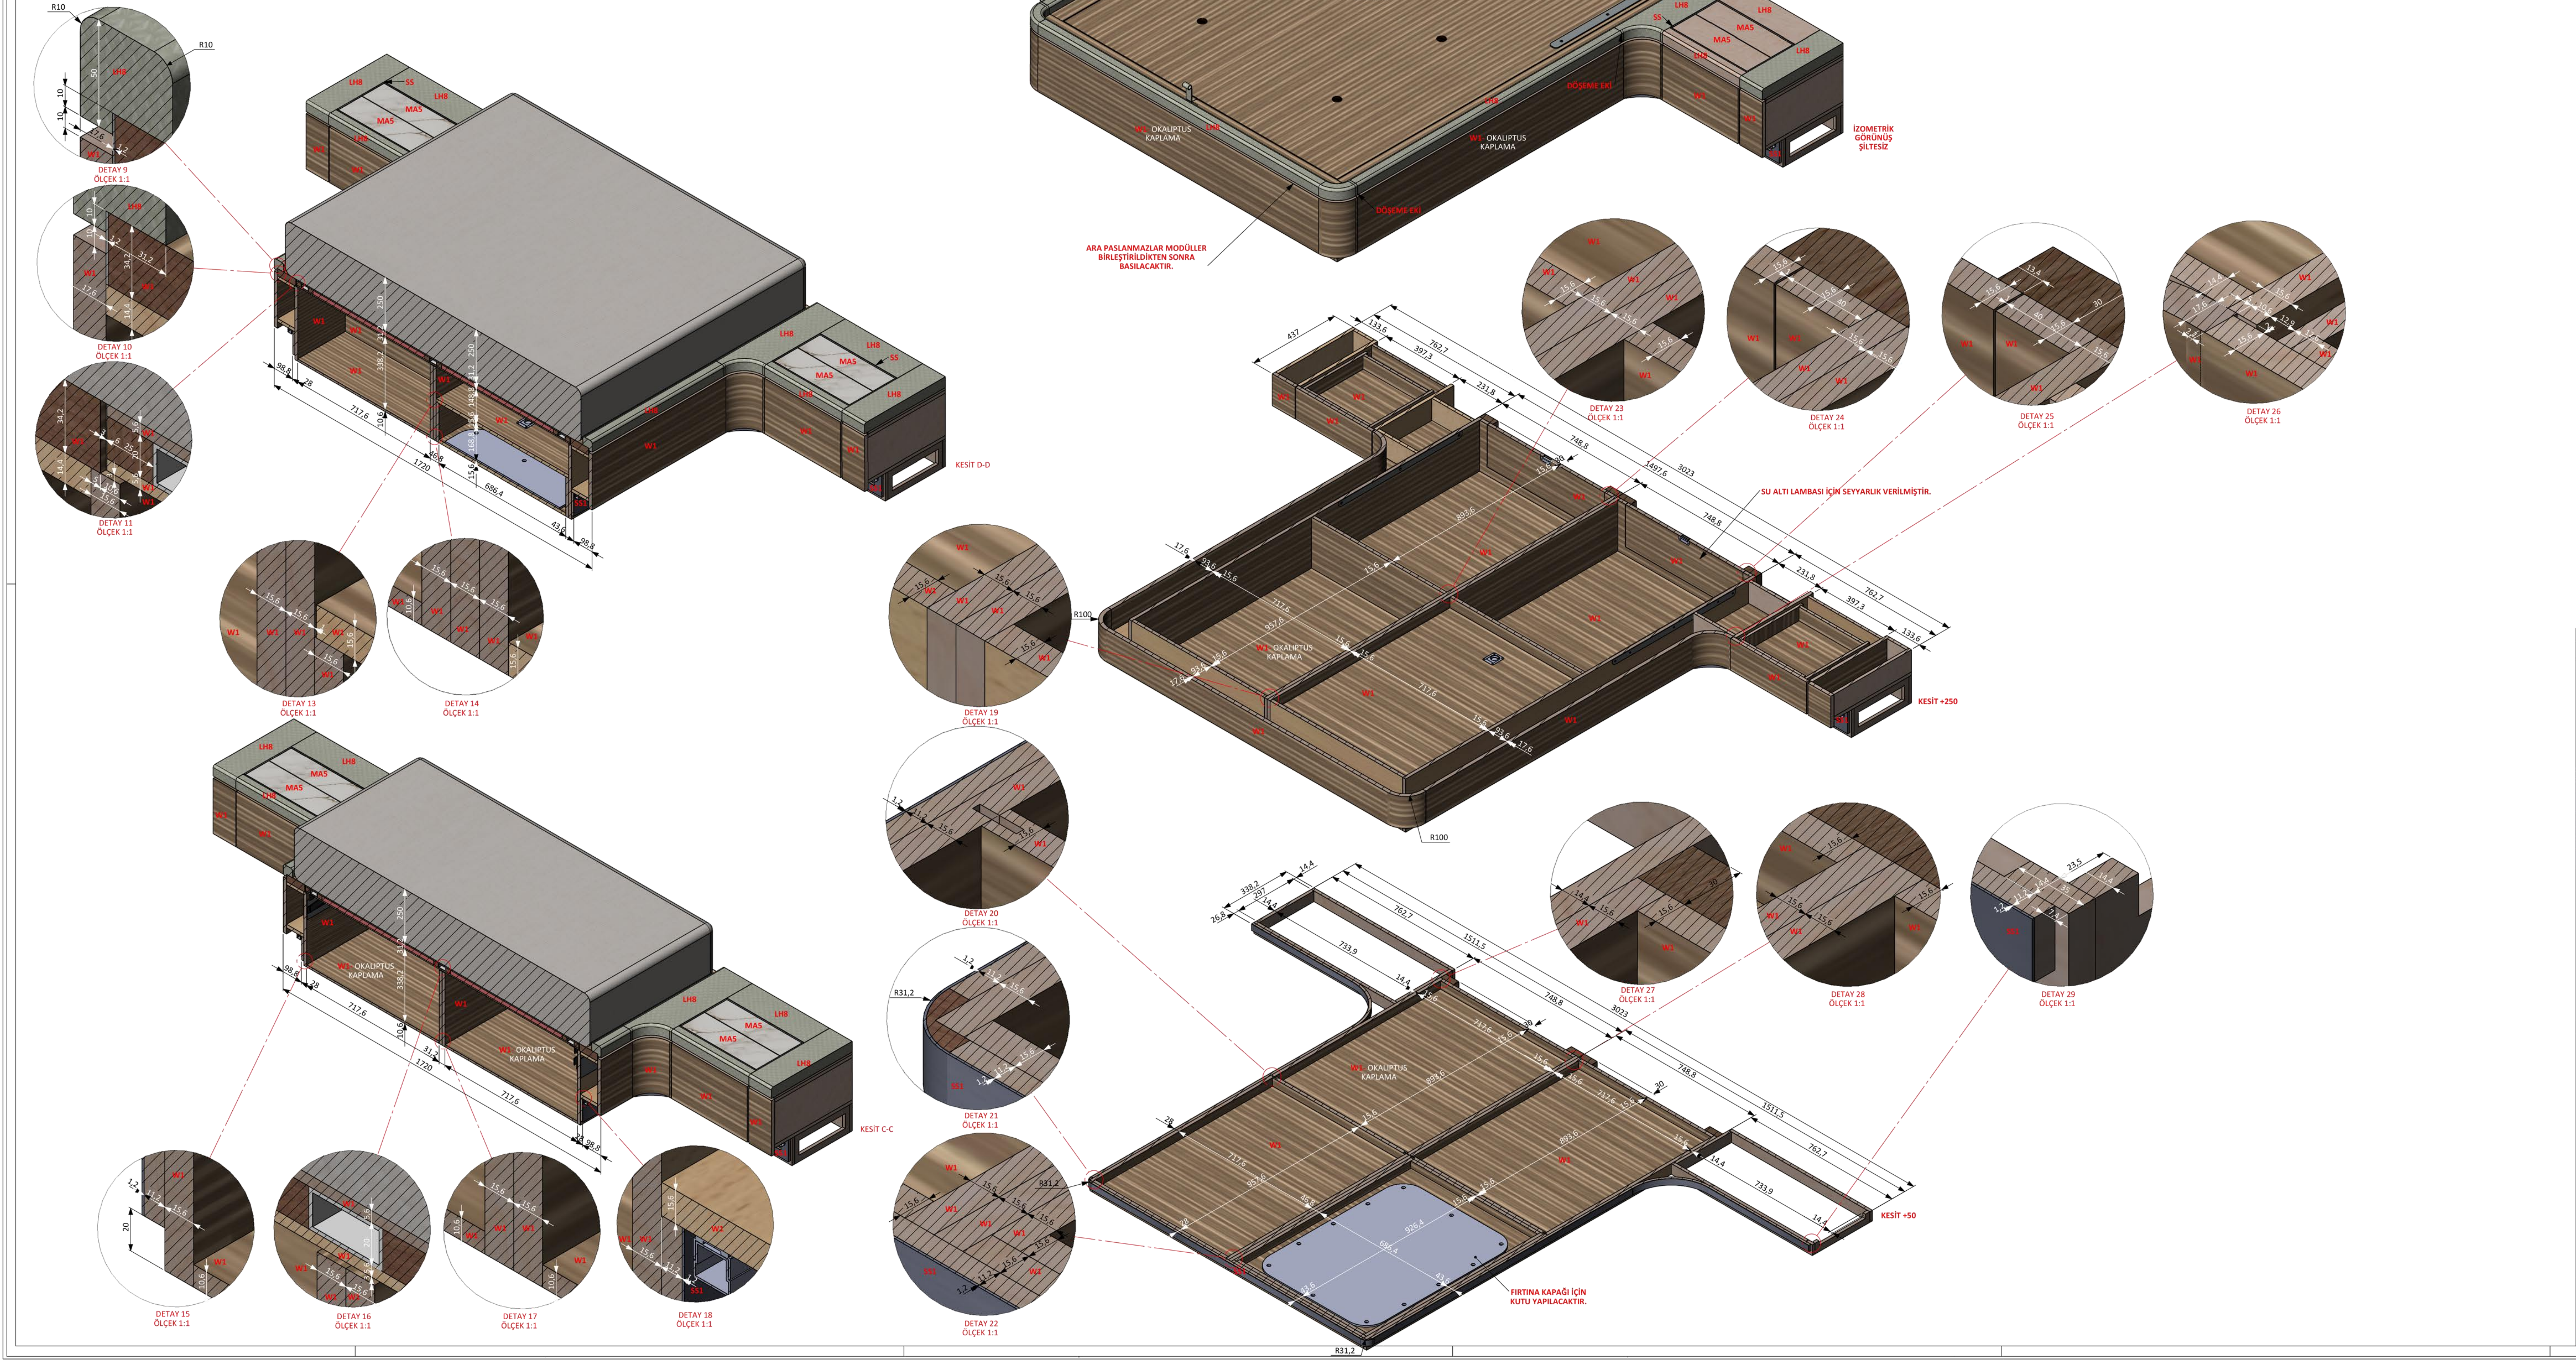

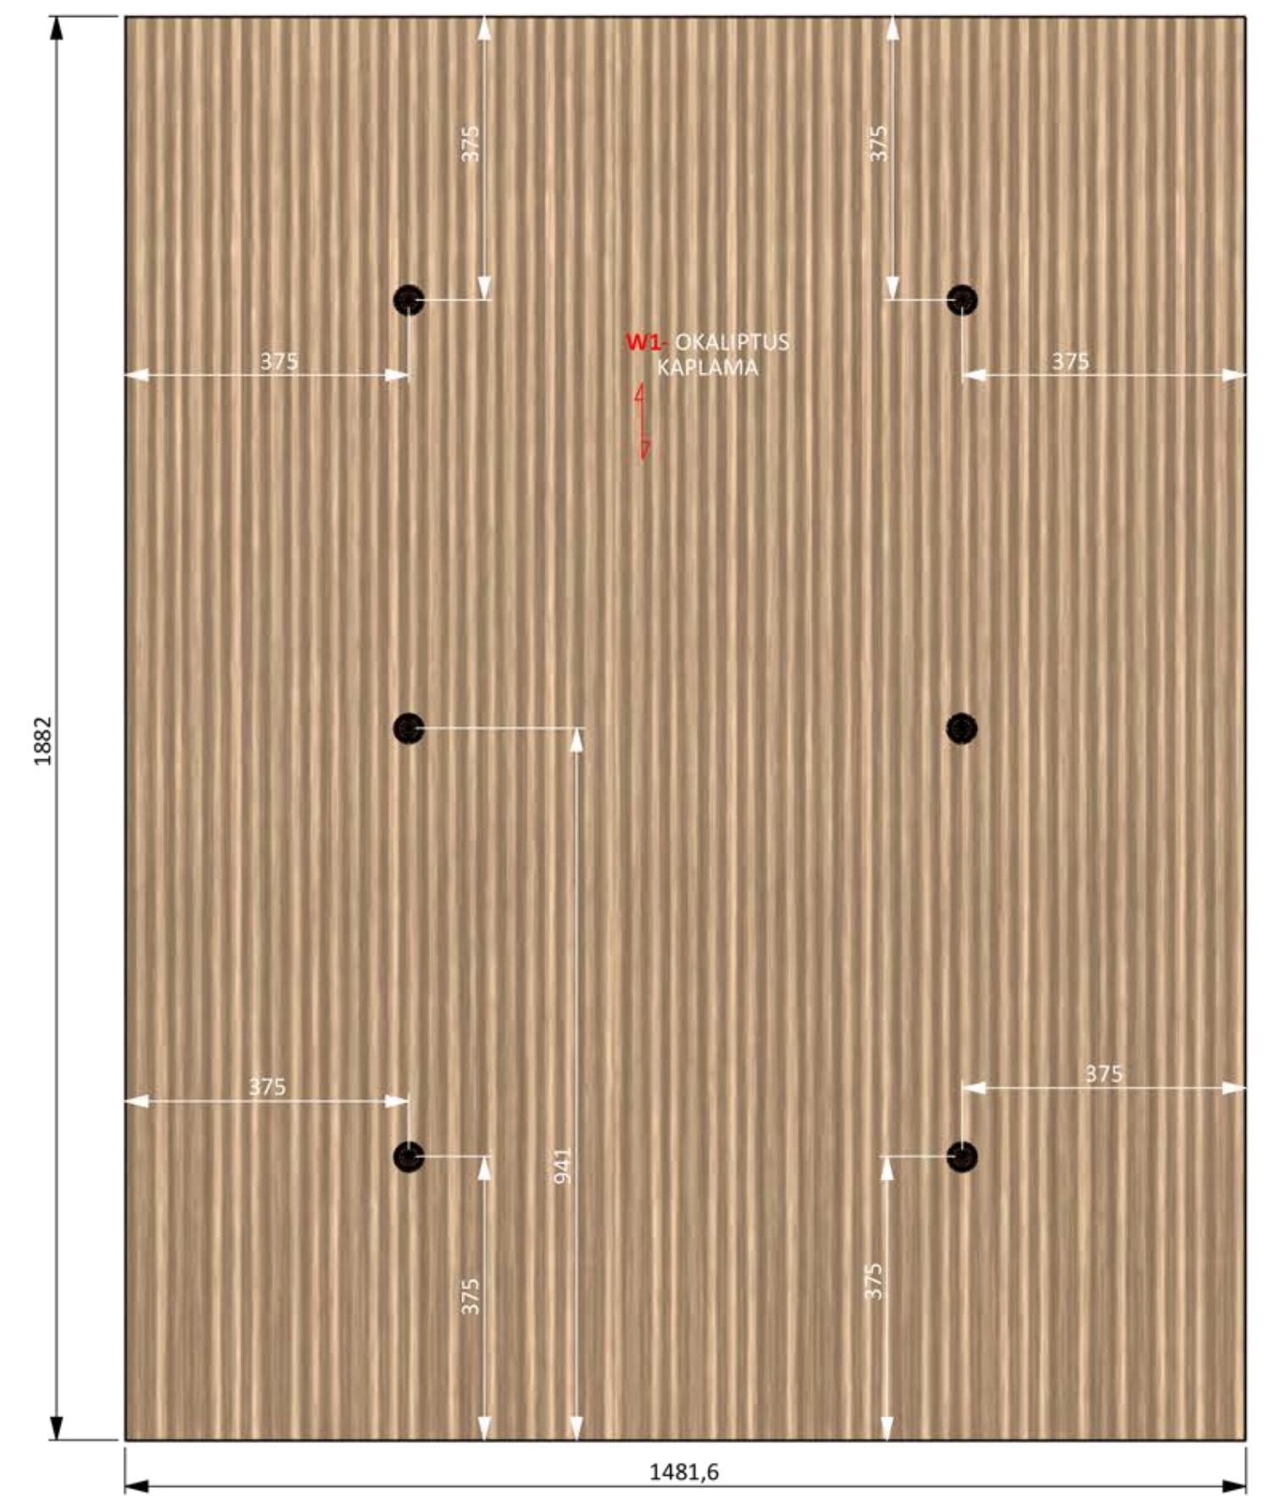

506-91/101 MİSAFİR KAMARA 202&204 YATAK KOMODİN İMALATI P1

REVİZYON / REVISIONS

REV.	TANIM	BY	TARİH	ONAY
A	İLK ÇIKTI	HALE D.	11.05.2026	

URETIM NOTLARI / NOTES OF PRODUCTION

-BU ÇİZİM 202 KABİNİNE AİTTİR 204 KABİNİNİN YATAĞI SİMETRİK OLARAK ÜRETİLECEKTİR.
-ARA PASLANMAZLAR MODÜLLER BİRLEŞTİKTEN SONRA BASILACAKTIR.
-FIRTINA KAPAĞI İÇİN KUTU YAPILACAKTIR.
-OKALİPTUS KAPLAMALI PARÇALARDA DESEN TAKİBİ VARDIR.
-KAPLAMA TAKİBİ OLAN PARÇALAR HAMDAN KESİLİP KABİN GENELİYLE BİRLİKTE KAPLAMALARI DESEN TAKİBİ AYARLANIP BASILACAKTIR.
-MONTAJA İKİ MODÜL OLARAK GÖNDERİLECEKTİR.
-FUGALARA MASİF GÖMÜLECEKTİR.
-ÇEKMECELERE GRABER KİLİT YERİNE MIKTANIS TAKILACAKTIR.KOMODİN PROJESİ AYRI OLARAK VERİLMİŞTİR.
-DÖŞEME PAYI NUMUYE GÖRE DÜŞÜLECEKTİR.
-SU ALTI LAMBASI İÇİN SEYYARLIK VERİLMİŞTİR.
-KOMODİNLER SOL-SAĞ SİMETRİKTİR.
-KOMODİN ÜSTÜNDE PRİZLER , KEYPAD VE KABLOSUZ ŞARJ CİHAZI İÇİN GEREKLİ YERLER AÇILMIŞTIR.BU CİHAZLARA ULAŞIM İÇİN KOMODİN İÇLERİNE MÜDAHALE KAPAKLARI KONULACAKTIR.

AKSESUAR LİSTESİ /ACCESSORIES LIST

REF NO	BİRİM	TİP	PARÇA ADI	ADET
		AKSESUAR	ŞİLTE MENFEZİ_ALBATUR 141-0620-1670 KAHVERENGİ_V2	12
		AKSESUAR	FARŞ KULBU 65X55 - DEKA - 3913012_V2	3
		AKSESUAR	FASTMOUNT_PC-RF1_V2	8
		AKSESUAR	DERİ KULP_LH8	1
		AKSESUAR	YATAK MEKANIZMASI_1000N PİSTON_6276272290270_V2	1

-BU AKSESUARLAR ***İSKELE YATAĞINA*** AİTTİR. ***SANCAK KABİNİ*** İÇİNDE AYNI MİKTARDA AKSESUAR KULLANILACAKTIR.

MALZEME LEJANTI / MATERIAL LEGEND

▨	W1- OKALIPTUS KAPLAMA
▨	LH8-TBD DERI/ LEATHER
▨	SS1-FIRÇALI PASLANMAZ /BRUSHED STAINLESS STEEL

ILGILI CIZIMLER /RELATED DRAWINGS

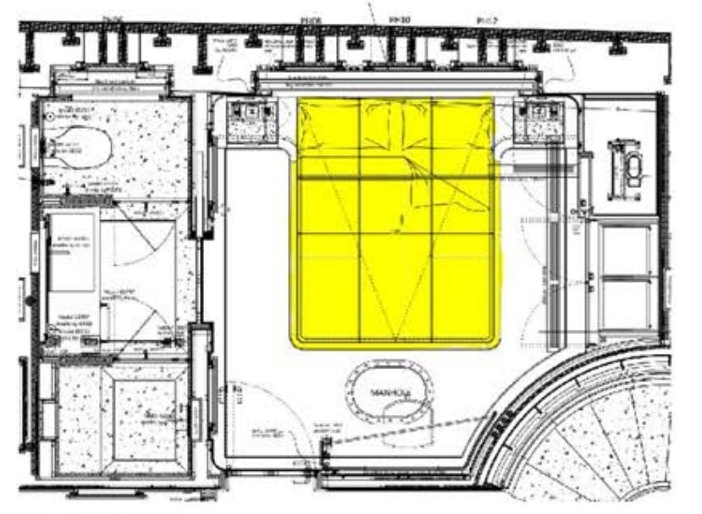

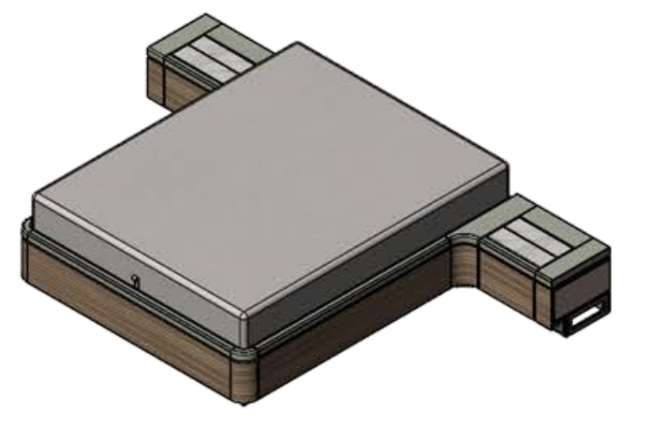

SEPTEMAR MOBİLYA VE YAT SAN. TİC. LTD. ŞTİ.
Balçık Mah. 3275. Sokak No:9 Gebze / KOCAELİ
Tel: +90 262 751 30 83 Fax: +90 262 751 30 82
www.septemar.com e-mail: info@septemar.com

Proje adı: NB84 50m BİLGİN Project name: NB84 50m BİLGİN	Tasarım: Hotlab Design:Hotlab	Çizen: Hale Demirpehlivan Drawing : Hale Demirpehlivan
Güverte: Alt Güverte Deck: Lower Deck	Ölçekler: 1/10 Scales: 1/10	Pafta adı: 506-91/101 Misafir Kamara 202&204 Yatak Komodin İmalatı Drawing name: 506-91/101 Guest Cabins 202&204 Beds Production
Kamara: Misafir Kamara 202 Room: Misafir Kamara 202	Tarih:11.05.2026 Date:11.05.2026	Pafta No: 2/1 (A0) Sheet Number: 2/1 — İş emri no: 506-91/101 Work order number: 506-91/101